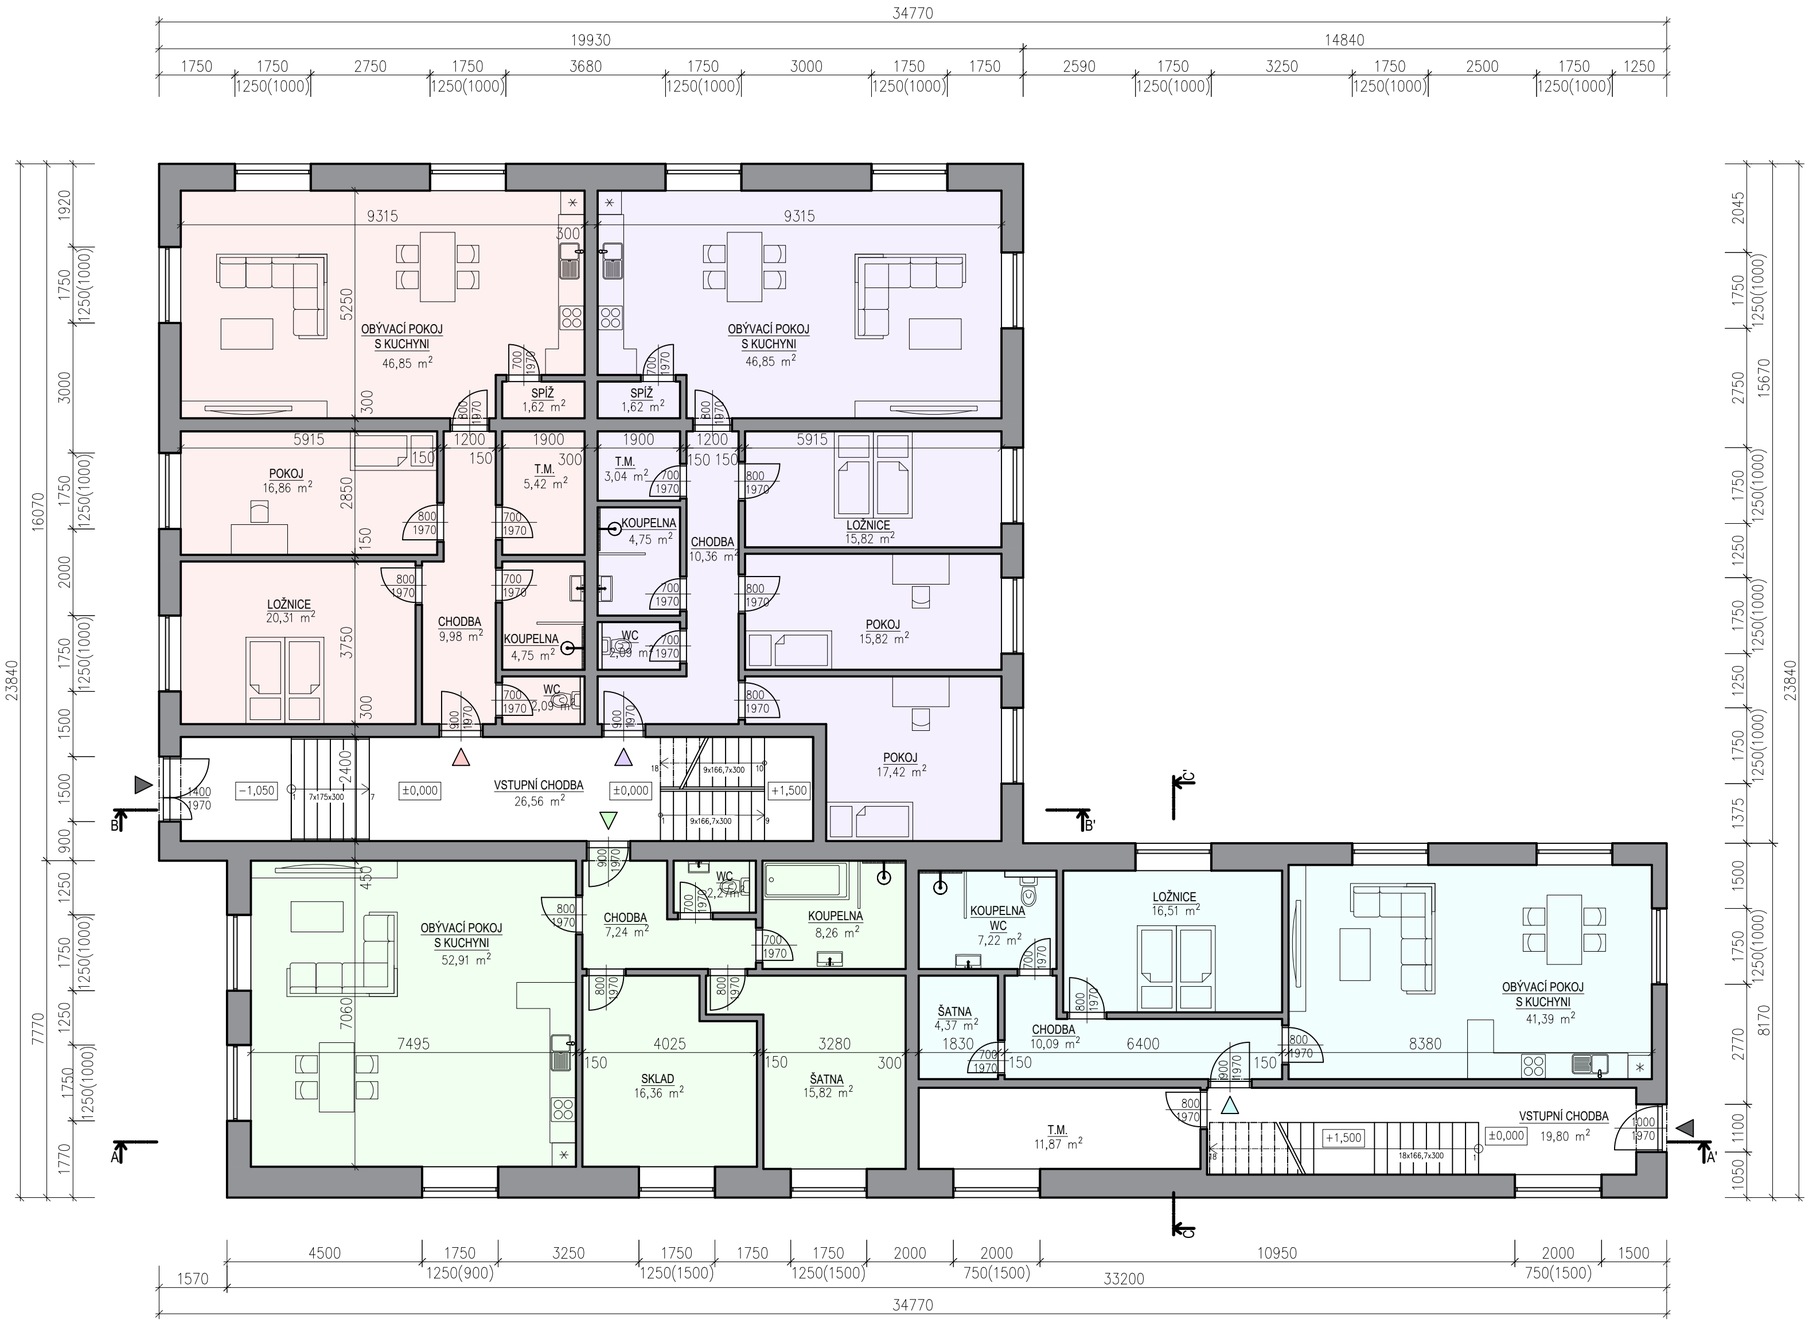


LEGENDA MÍSTNOSTÍ

Č. B.	NÁZEV	m2	PODLAHA	STĚNY	STROP
BYT Č.1 (3+KK)	CHODBA	9,98	LAMINÁT. POD.	VÁP.OMÍTKA	SDK + 2x MALBA
	OBÝVACÍ POKOJ S KUCHYNÍ	46,85	LAMINÁT. POD.	VÁP.OMÍTKA	SDK + 2x MALBA
	SPÍŽ	1,62	LAMINÁT. POD.	VÁP.OMÍTKA	SDK + 2x MALBA
	POKOJ	16,86	LAMINÁT. POD.	VÁP.OMÍTKA	SDK + 2x MALBA
	LOŽNICE	20,31	LAMINÁT. POD.	VÁP.OMÍTKA	SDK + 2x MALBA
	T.M.	5,42	KERAM. DLAŽBA	VÁP.OMÍTKA	SDK + 2x MALBA
	KOUPELNA	4,75	KERAM. DLAŽBA	VÁP.OM. + KER. OBKLAD	SDK + 2x MALBA
	WC	2,09	KERAM. DLAŽBA	VÁP.OM. + KER. OBKLAD	SDK + 2x MALBA
	CELKEM:	**107,88**			
BYT Č.2 (4+KK)	CHODBA	10,36	LAMINÁT. POD.	VÁP.OMÍTKA	SDK + 2x MALBA
	OBÝVACÍ POKOJ S KUCHYNÍ	46,85	LAMINÁT. POD.	VÁP.OMÍTKA	SDK + 2x MALBA
	SPÍŽ	1,62	LAMINÁT. POD.	VÁP.OMÍTKA	SDK + 2x MALBA
	LOŽNICE	15,82	LAMINÁT. POD.	VÁP.OMÍTKA	SDK + 2x MALBA
	POKOJ	15,82	LAMINÁT. POD.	VÁP.OMÍTKA	SDK + 2x MALBA
	POKOJ	17,42	LAMINÁT. POD.	VÁP.OMÍTKA	SDK + 2x MALBA
	T.M.	3,04	KERAM. DLAŽBA	VÁP.OMÍTKA	SDK + 2x MALBA
	KOUPELNA	4,75	KERAM. DLAŽBA	VÁP.OM. + KER. OBKLAD	SDK + 2x MALBA
	WC	2,09	KERAM. DLAŽBA	VÁP.OM. + KER. OBKLAD	SDK + 2x MALBA
	CELKEM:	**117,77**			
BYT Č.3 (3+KK)	CHODBA	7,24	LAMINÁT. POD.	VÁP. OMÍTKA	SDK + 2x MALBA
	OBÝVACÍ POKOJ S KUCHYNÍ	52,91	LAMINÁT. POD.	VÁP. OMÍTKA	SDK + 2x MALBA
	SKLAD	16,36	LAMINÁT. POD.	VÁP. OMÍTKA	SDK + 2x MALBA
	WC	2,27	KERAM. DLAŽBA	VÁP.OM. + KER. OBKLAD	SDK + 2x MALBA
	KOUPELNA	8,26	KERAM. DLAŽBA	VÁP.OM. + KER. OBKLAD	SDK + 2x MALBA
	CELKEM:	**105,86**			
BYT Č.4 (2+KK)	CHODBA	10,09	LAMINÁT. POD.	VÁP. OMÍTKA	SDK + 2x MALBA
	OBÝVACÍ POKOJ S KUCHYNÍ	41,39	LAMINÁT. POD.	VÁP. OMÍTKA	SDK + 2x MALBA
	LOŽNICE	16,51	LAMINÁT. POD.	VÁP. OMÍTKA	SDK + 2x MALBA
	KOUPELNA S WC	7,22	KERAM. DLAŽBA	VÁP.OM. + KER. OBKLAD	SDK + 2x MALBA
	ŠATNA	4,37	LAMINÁT. POD.	VÁP. OMÍTKA	SDK + 2x MALBA
	CELKEM:	**79,58**			